

SURVEYOR'S NOTE:


1. BASIS OF BEARING IS THE TEXAS COORDINATE SYSTEM, CENTRAL ZONE (4203), NAD83
2. DISTANCES SHOWN HEREON ARE BASED ON SURFACE MEASUREMENTS. TO CONVERT SURFACE DISTANCES TO GRID, MULTIPLY BY THE COMBINED SCALE FACTOR.
3. ALL EASEMENTS OF RECORD ARE SHOWN OR NOTED ON THE PLAT AS FOUND ON THE TITLE POLICY OR DISCOVERED WITH A TITLE SEARCH PREPARED FOR THE MOST RECENT PURCHASE OF PROPERTY. IN ADDITION TO THE EASEMENTS SHOWN HEREON, THERE ARE NO FURTHER EASEMENTS ARE FOUND AFTER THE SALE.
4. LOT 17 AND LOT 18 WILL HAVE DRIVEWAYS ONTO NAPOLI TOSCANA CT ONLY AND GOING TO HAVE MASONRY WALL ALONG THE REAR PROPERTY LINE.
5. THE COMBINED SCALE FACTOR FOR THIS PROJECT IS 0.999908769

BENCHMARK LIST: -- NAVD88 -- GEOID 12

BM #1:
MAG NAIL IN THE CURB INLET ALONG OSAGE DRIVE
N: 10183176.34, E: 3074043.57, ELEV = 993.97 FEET

BM #2:
MAG NAIL IN THE CURB INLET ALONG OSAGE DRIVE
N: 10182851.23, E: 3073230.404, ELEV = 997.96 FEET

NOTE: A PERPETUAL PUBLIC SAFETY AND PUBLIC SERVICE EASEMENT IS HEREBY DEDICATED FOR THE PURPOSE OF PROVIDING PUBLIC SAFETY SERVICES, POLICE, FIRE AND MEDICAL SERVICES, UTILITY METER READING, CODE ENFORCEMENT, BUILDING INSPECTIONS, SOLID WASTE COLLECTION, PUBLIC SCHOOL, TRANSPORTATION, ANY OTHER PUBLIC SERVICES AND ENFORCING THE CITY ORDINANCES AND GIVING THE CITY AND ITS AUTHORIZED OFFICERS AND DESIGNEES UNINHIBITED INGRESS AND EGRESS OVER, ACROSS AND THROUGH SUCH STREETS, ROADWAYS, AND RIGHTS-OF-WAY FOR THE PURPOSE OF PROVIDING PUBLIC SAFETY SERVICES, POLICE, FIRE AND MEDICAL SERVICES, AND ENFORCING THE PENAL CODE AND CITY ORDINANCES. THE HOA SHALL MAINTAIN AT ALL TIMES WITH THE CITY SECRETARY THE CURRENT GATE CODE OR KEY FOR ALL GATES REGULATING ACCESS TO AND FROM THE SUBDIVISION.

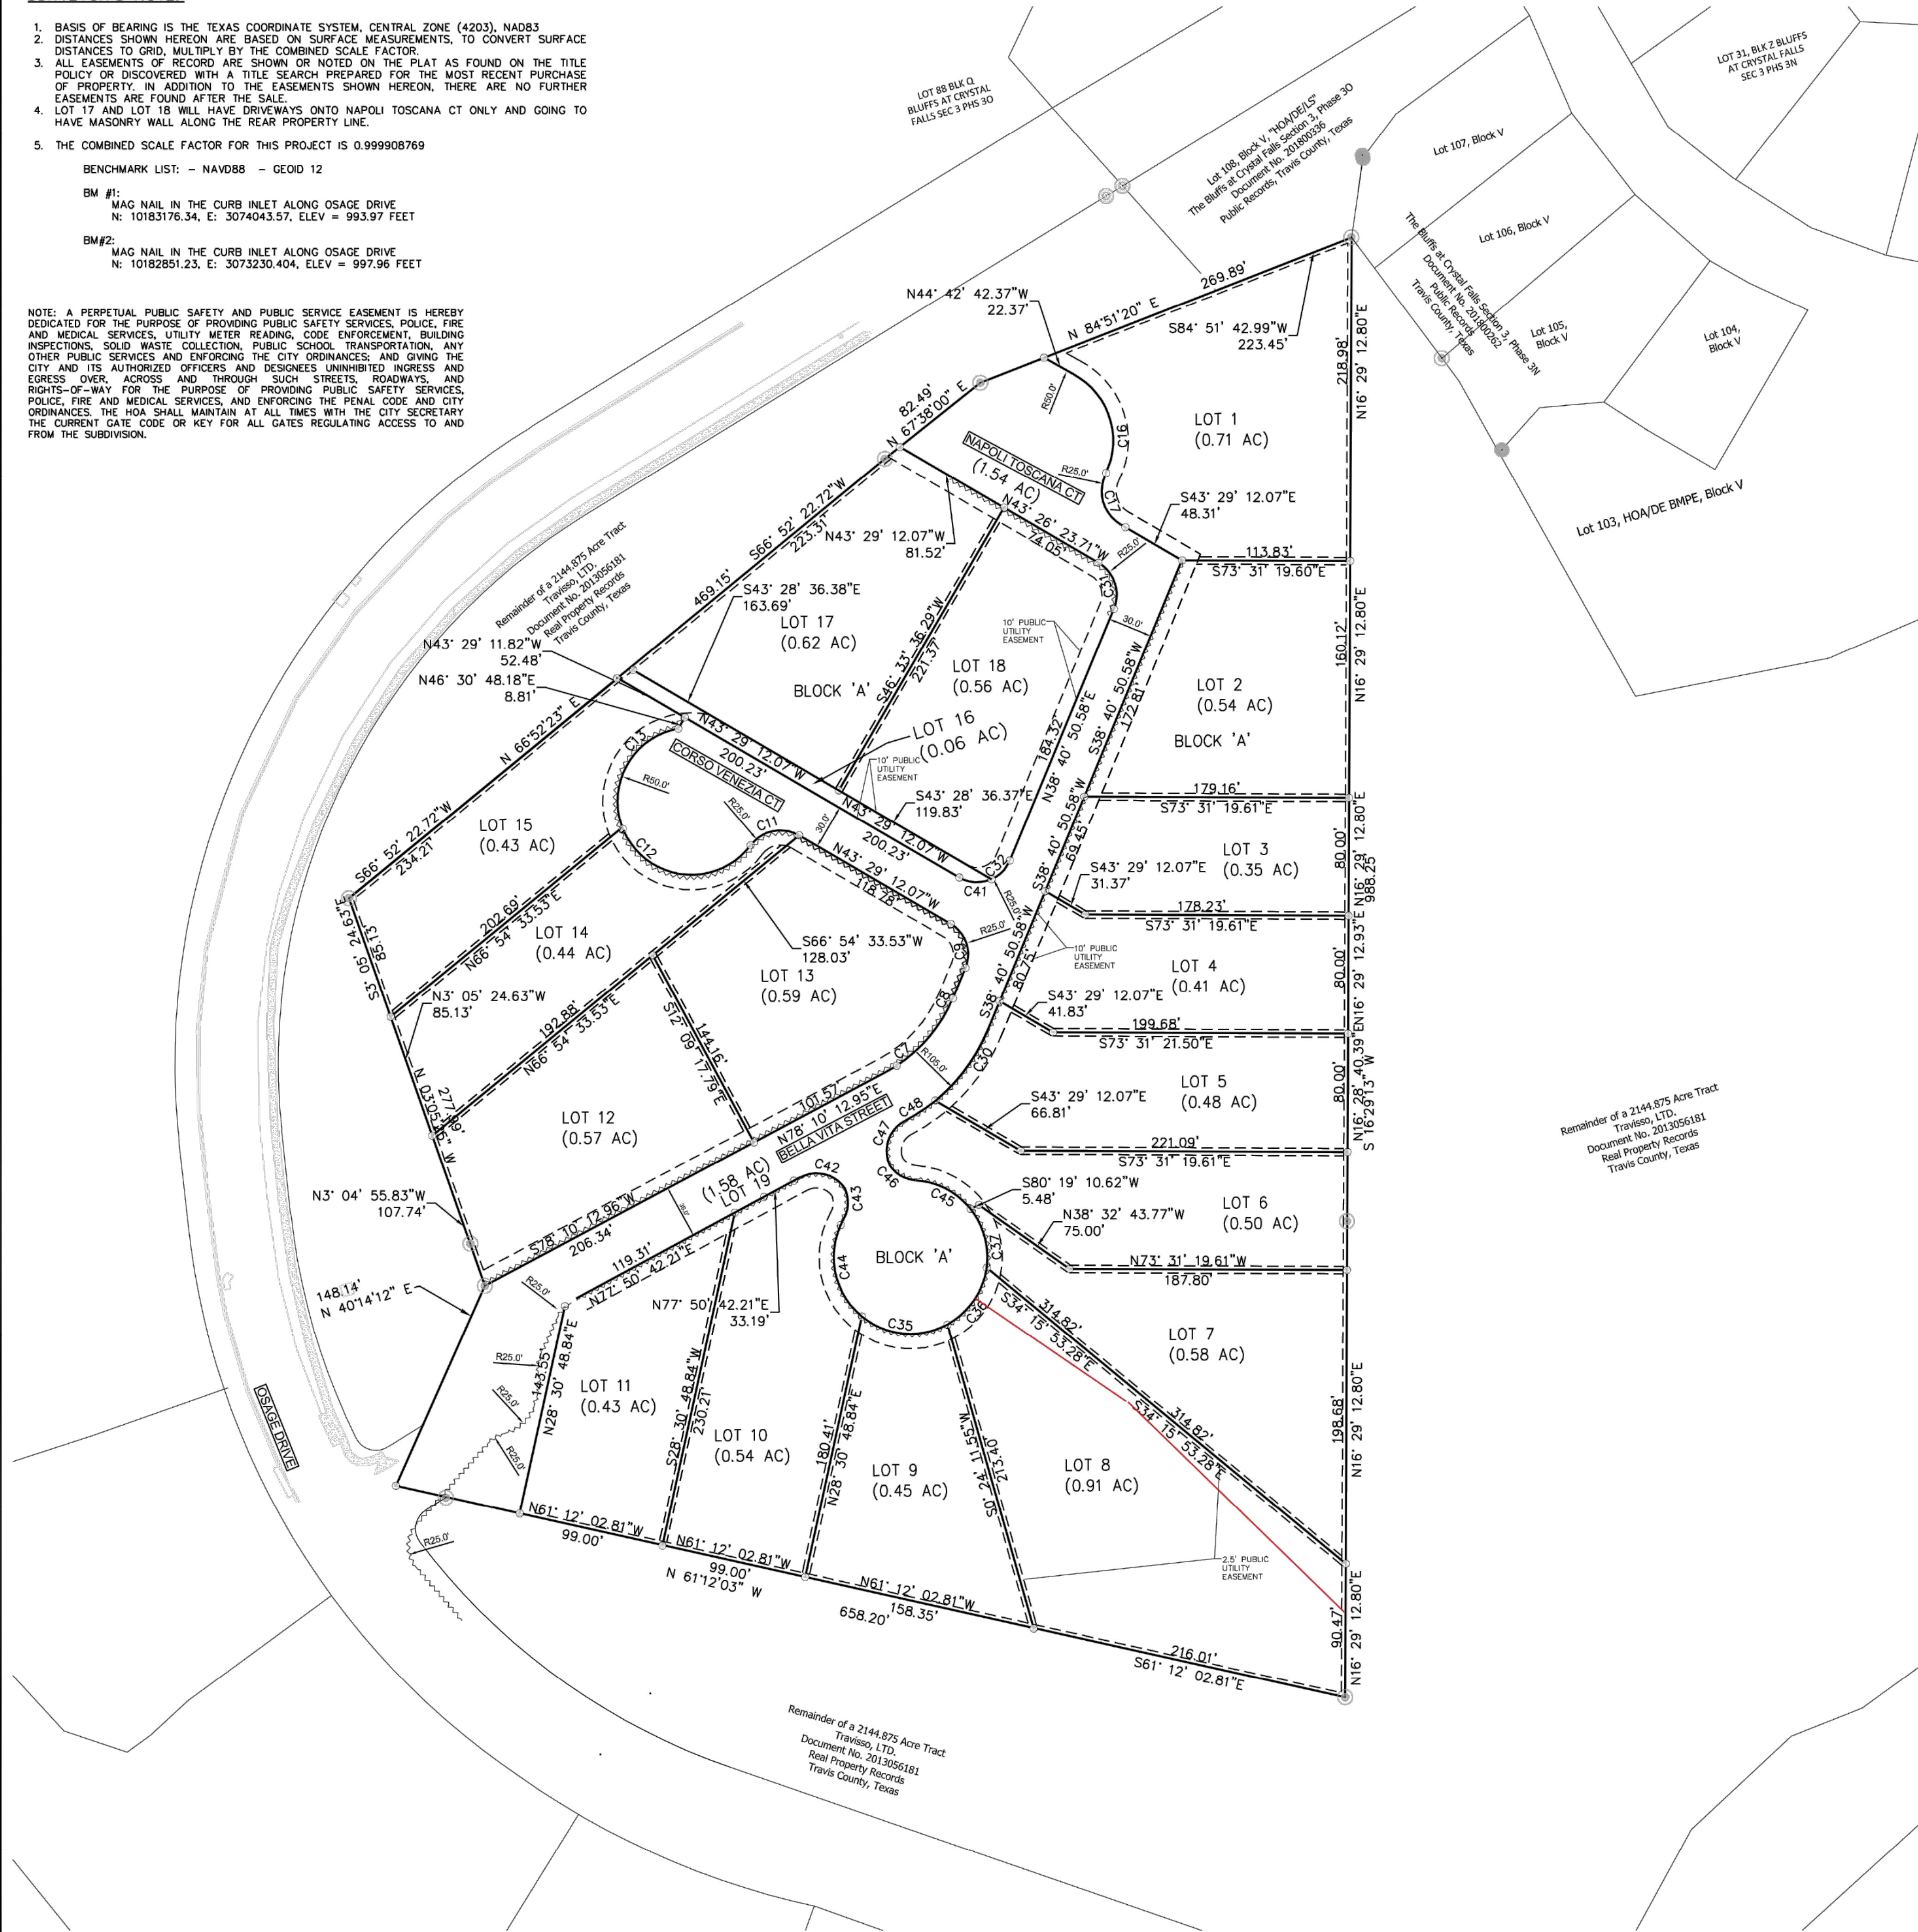

Curve Table					
Curve #	Length	Radius	Delta	Chord Direction	Chord Length
C7	68.23	99.00	39.49	N58° 25' 32"E	66.89
C8	68.23	99.00	39.49	N58° 25' 32"E	66.89
C9	34.42	24.00	82.17	N2° 24' 11"W	31.54
C11	36.53	25.00	83.72	S85° 20' 40"E	33.36
C12	107.12	50.00	122.75	S65° 49' 47"E	87.78
C13	87.62	50.00	100.40	N45° 44' 36"E	76.83
C16	76.65	50.75	86.54	S1° 27' 06"E	518.69
C17	24.55	25.82	54.48	S16° 09' 50"E	325.51
C30	59.37	120.00	28.35	S52° 51' 15"W	58.77
C31	35.85	25.00	82.17	N2° 24' 11"W	32.86
C32	18.23	24.00	43.52	N60° 26' 23"E	17.79
C35	61.80	52.00	68.09	S68° 25' 22"E	58.22
C36	48.42	52.00	53.35	S50° 51' 21"W	516.12
C37	38.77	52.00	42.71	S2° 49' 19"W	37.87
C41	22.75	24.00	54.31	N70° 38' 38"W	21.91
C42	34.41	23.00	85.71	S59° 18' 04"E	31.29
C43	21.47	23.00	53.48	S18° 52' 33"W	20.70
C44	46.64	52.00	51.39	S19° 55' 11"W	333.27
C45	43.03	52.00	47.41	N46° 13' 00"W	41.81
C46	21.48	23.00	53.51	N43° 10' 15"W	20.71
C47	34.84	23.00	86.78	N35° 29' 59"E	31.60
C48	24.84	135.34	10.52	N72° 57' 36"E	24.80

LOT SUMMARY TABLE


LOT NUMBER	ACREAGE	USE
LOT 1	0.71 ACRES	SINGLE FAMILY HOUSING
LOT 2	0.54 ACRES	SINGLE FAMILY HOUSING
LOT 3	0.35 ACRES	SINGLE FAMILY HOUSING
LOT 4	0.41 ACRES	SINGLE FAMILY HOUSING
LOT 5	0.48 ACRES	SINGLE FAMILY HOUSING
LOT 6	0.50 ACRES	SINGLE FAMILY HOUSING
LOT 7	0.58 ACRES	SINGLE FAMILY HOUSING
LOT 8	0.91 ACRES	SINGLE FAMILY HOUSING
LOT 9	0.45 ACRES	DETENTION POND
LOT 10	0.54 ACRES	SINGLE FAMILY HOUSING
LOT 11	0.43 ACRES	SINGLE FAMILY HOUSING
LOT 12	0.57 ACRES	SINGLE FAMILY HOUSING
LOT 13	0.59 ACRES	SINGLE FAMILY HOUSING
LOT 14	0.44 ACRES	SINGLE FAMILY HOUSING
LOT 15	0.43 ACRES	SINGLE FAMILY HOUSING
LOT 16	0.06 ACRES	LANDSCAPE LOT
LOT 17	0.62 ACRES	SINGLE FAMILY HOUSING
LOT 18	0.56 ACRES	SINGLE FAMILY HOUSING
LOT 19	1.54 ACRES	PRIVATE STREET ROW
TOTAL	10.756 ACRES	SINGLE FAMILY HOUSING

STREET TABLE

STREET NAME	LENGTH (LF)
BELLA VITA STREET	930.00
CORSO VENEZIA CT	261.00
NAPOLI TOSCANO CT	159.50


REV. NO.	DESCRIPTION	DATE

Notes:

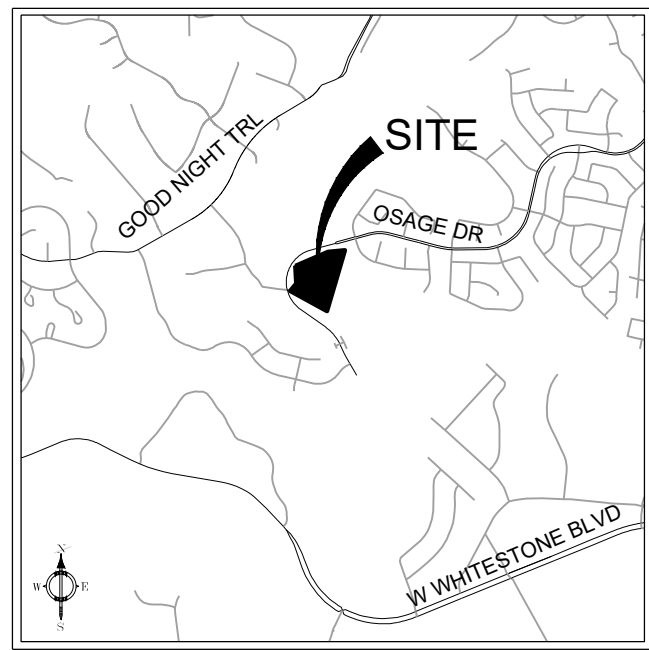

LEGEND

SIGNATURE/SEAL

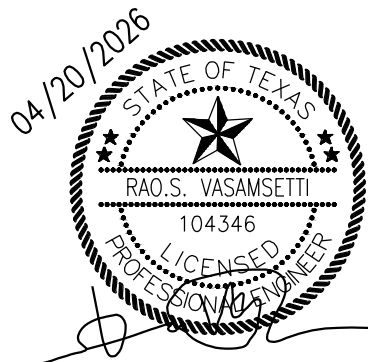

RCE RAO'S CONSULTING ENGINEERS

P.O. BOX 99291 SAN ANTONIO TX 78259
PHONE: 210.545.7587 FAX: 512.836.4555
www.raosconsulting.com

PROJECT DESCRIPTION:

VILLAS AT SPEAKING ROCK

TITLE:

APPROVED PRELIMINARY PLAT

DATE :	08/13/25	JOB NO.	2022-0727
DESIGNED BY :	RV	DRG NO.	7 OF 40
DRAWN BY :	PK		
CHECKED BY :	RV		